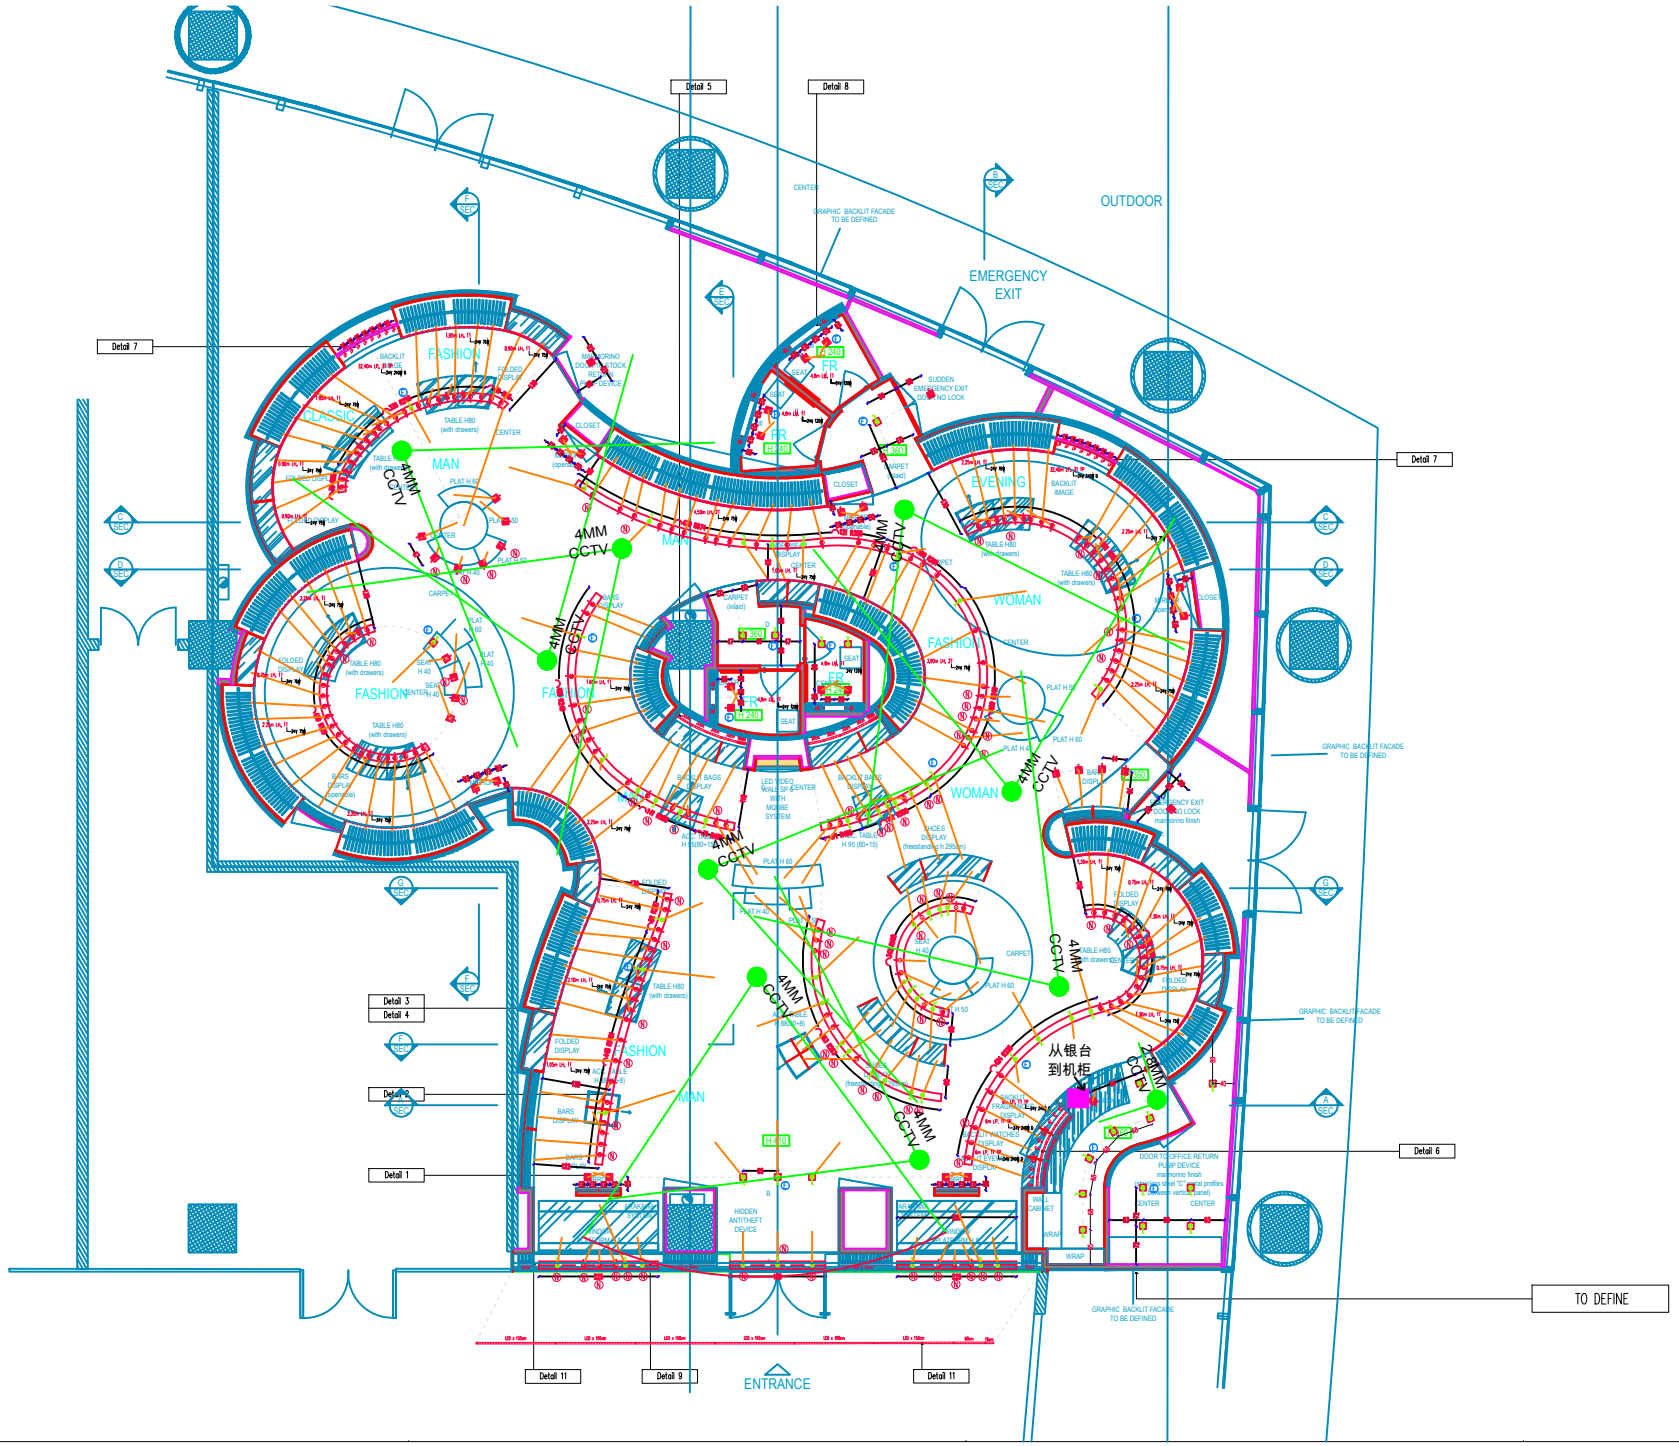

BB LD BARBARA BALESTRERI LIGHTING DESIGN

Via Paganini, 3 - 20131, Milano, Italia - Tel. +39 02 20240645 - Fax. +39 02 2024 1137
@ info@balestreri-lighting.it web: www.balestreri-lighting.it

Progetto/Project: EA_SHENYANG MIXC	Oggetto/Object: DEFINITIVE LAYOUT UP2	Disegno/Drawing: PLAN
Data inizio/Original date: 20/04/2016	Ultimo aggiornamento/Last update: 04/07/2016	aggiornamenti precedenti/previous updates: 28/04/2016 22/06/2016 27/06/2016
Scala A1/Scale A1: 1:50	Scala A3/Scale A3: 1:100	
Progettista architettonico/Architectural designer: Studio Cipriani (Layout received on: 01/07/2016)	Progettista illuminotecnico/Lighting designer: MB	n° tavola/n° Layout: 1

ALL MEASUREMENTS TO BE VERIFIED ON SITE